


4 鉄骨鉄筋コンクリート構造の耐震計算

出題:H18

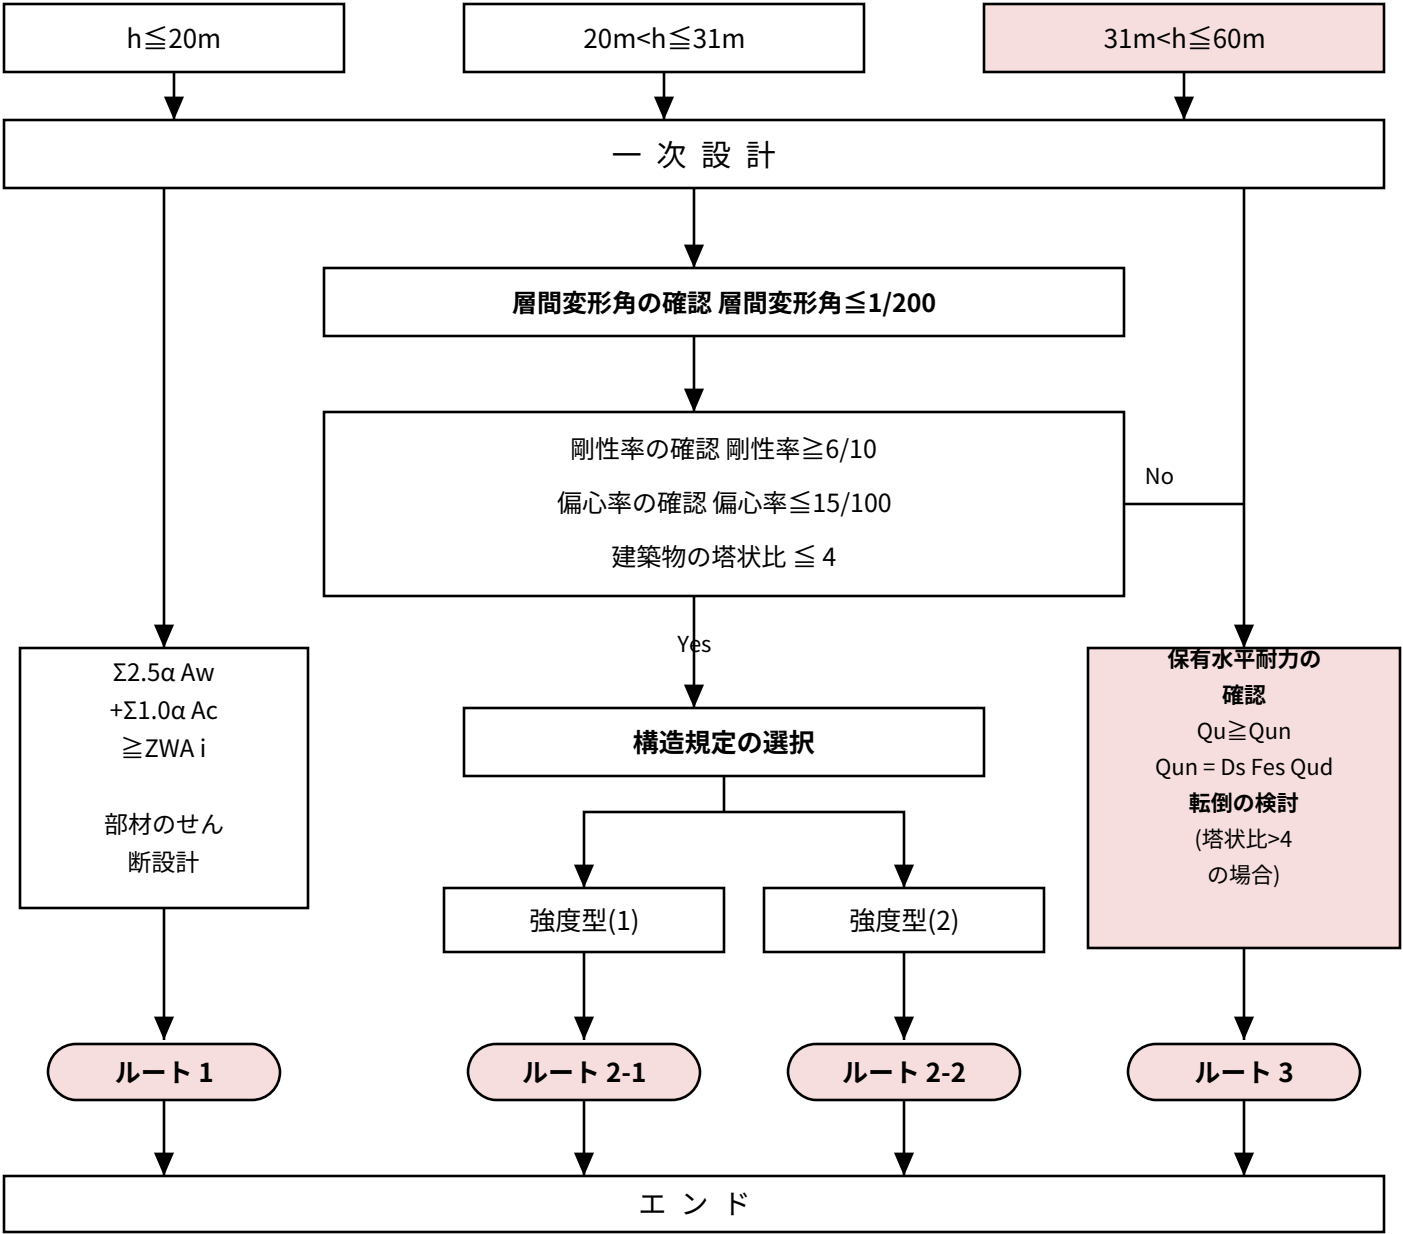

鉄骨鉄筋コンクリート造建築物の耐震計算フロー

h:建築物の高さ